



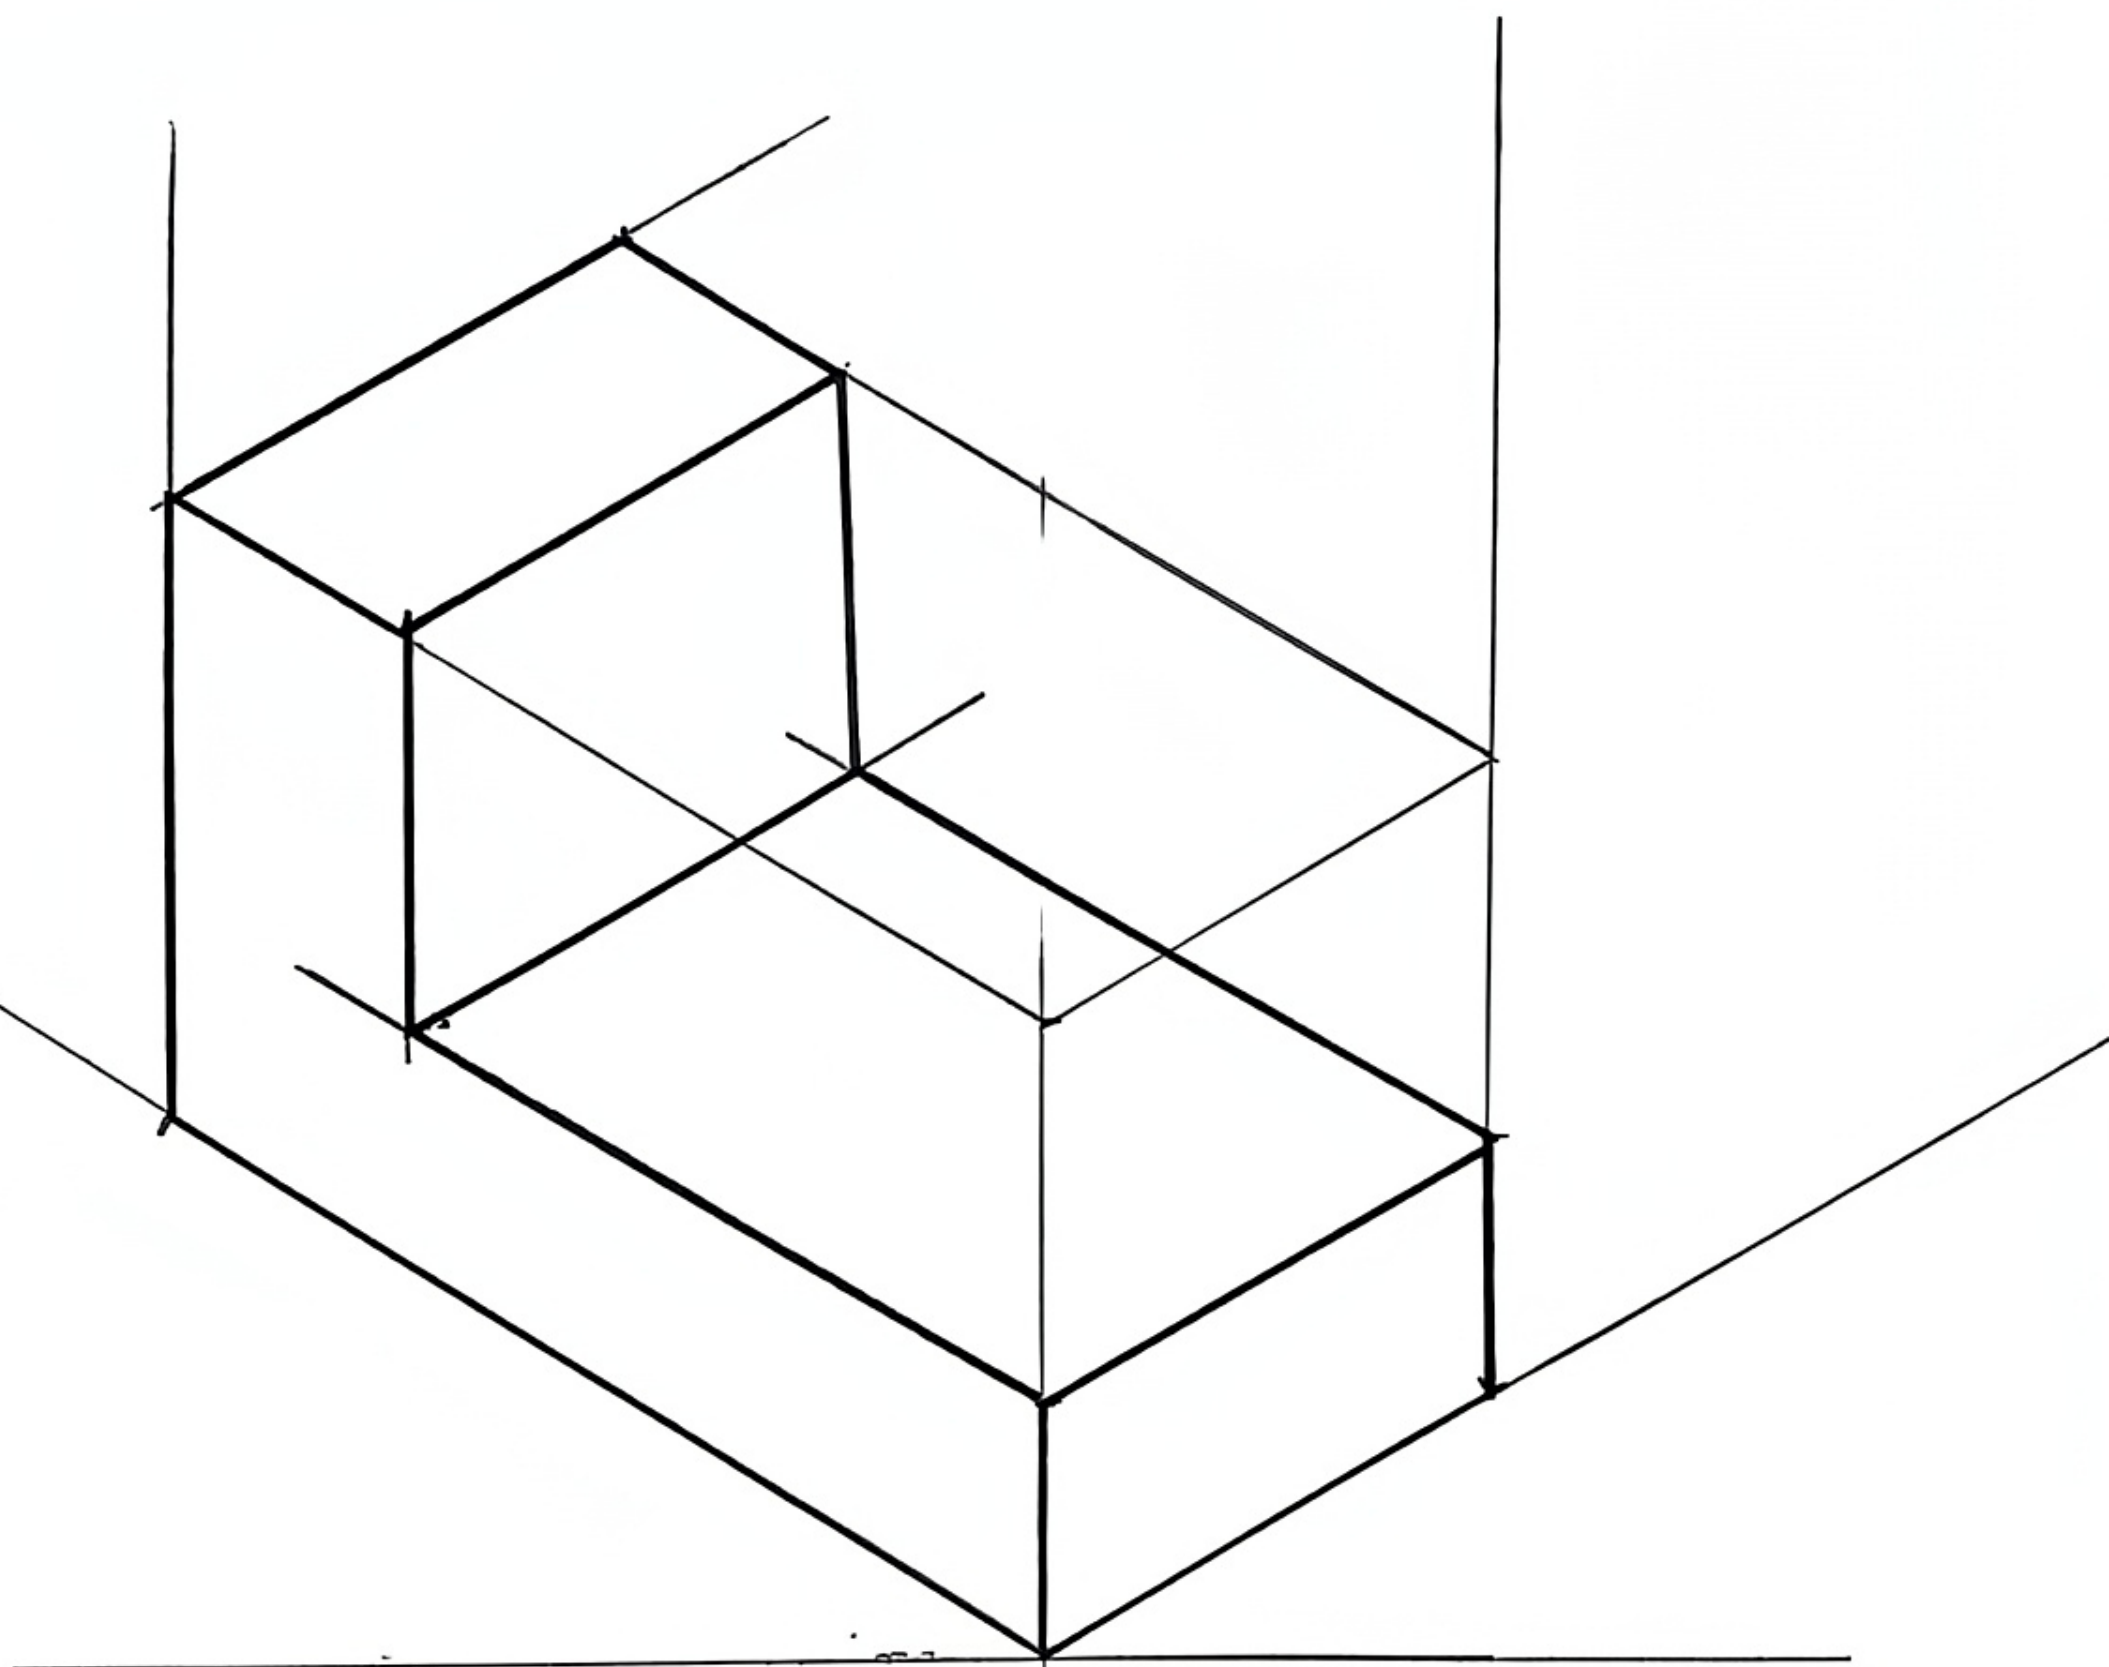

UNIDADES	DIBUJADO	HENRY OBREGON BRAVO	UTP
m. m	REVISADO	RIVERA VALE SANDRO	
ESCALA	FECHA	12-09-26	UNIVERSIDAD TECNOLÓGICA DEL PERÚ
1:1	LAMINA	PROYECCIONES ISO METRICAS DEFINICION y TIPOS	Nº: PLANO. 1/2

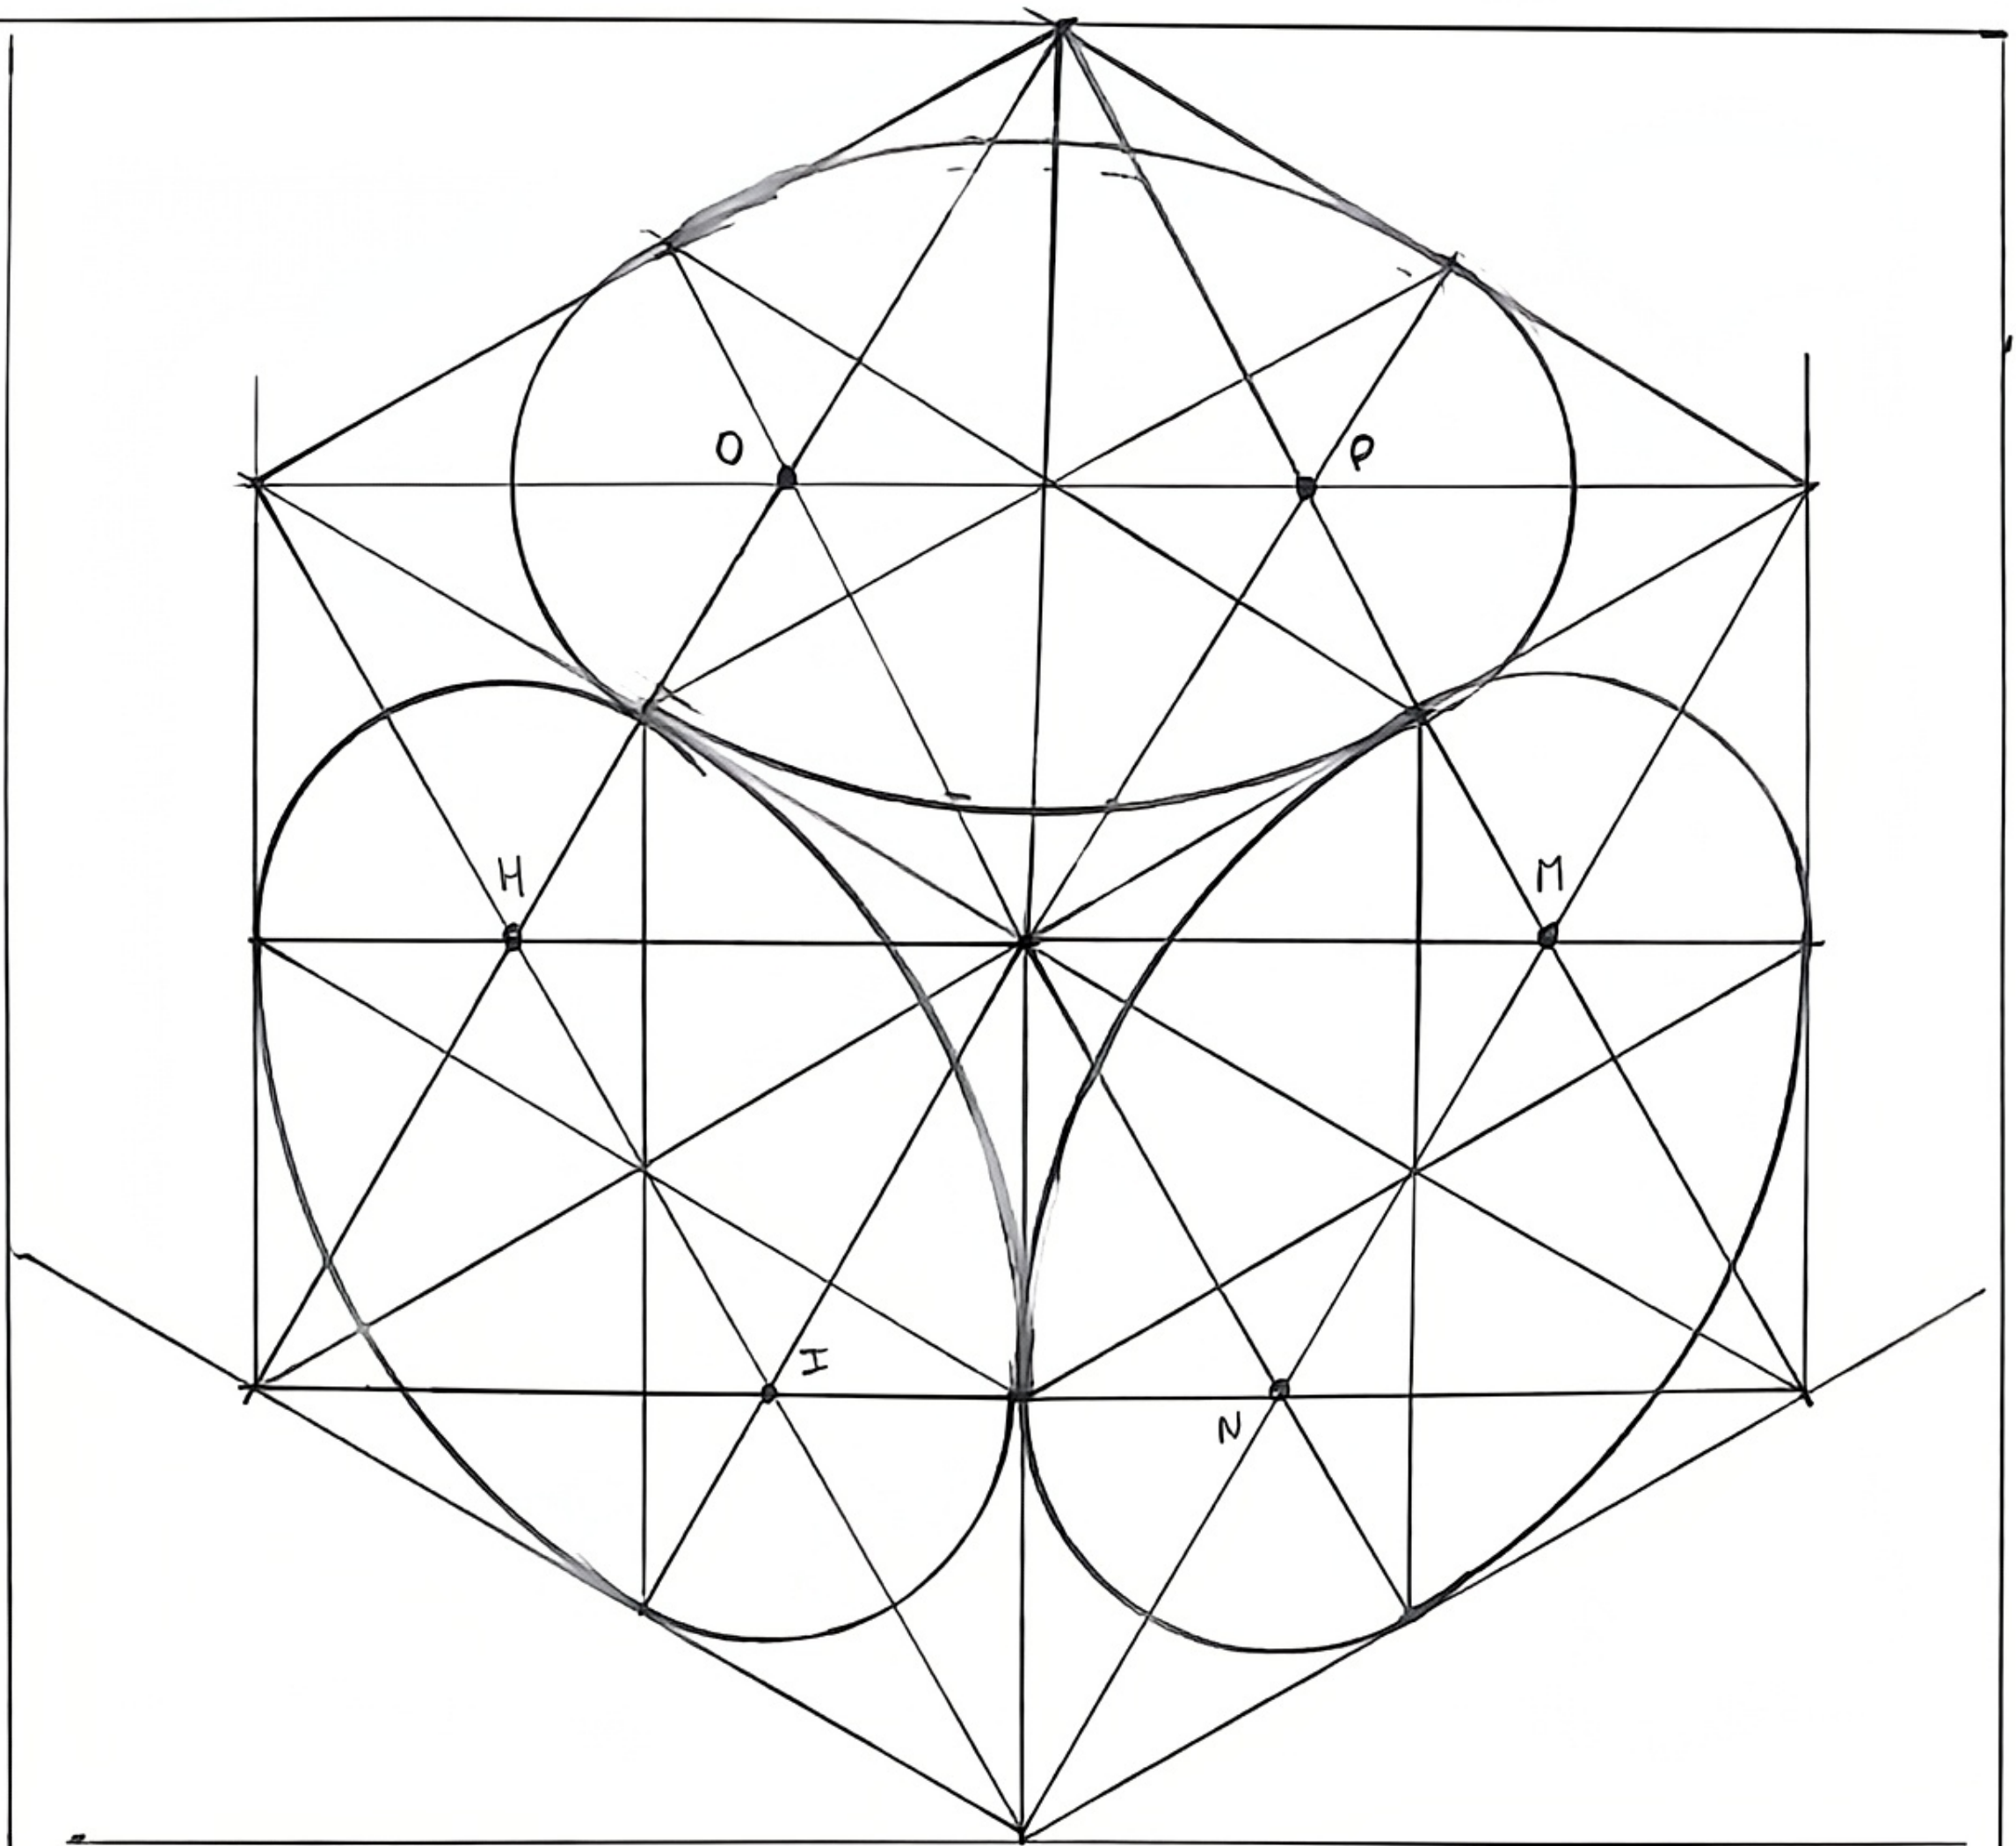

UNIDADES	DIBUJADO	HENRY OBREGON BRAVO	UTP	
M.M	REVISADO	RIVERA VALLE SANDRO	UNIVERSIDAD TECNOLÓGICA DEL PERÚ	
ESCALA	FECHA	12-09-26	N: PLANO	
1:1	LAMINA	PROYECCIONES ISO METRICAS DEFINICION y TIPOS	2/2	